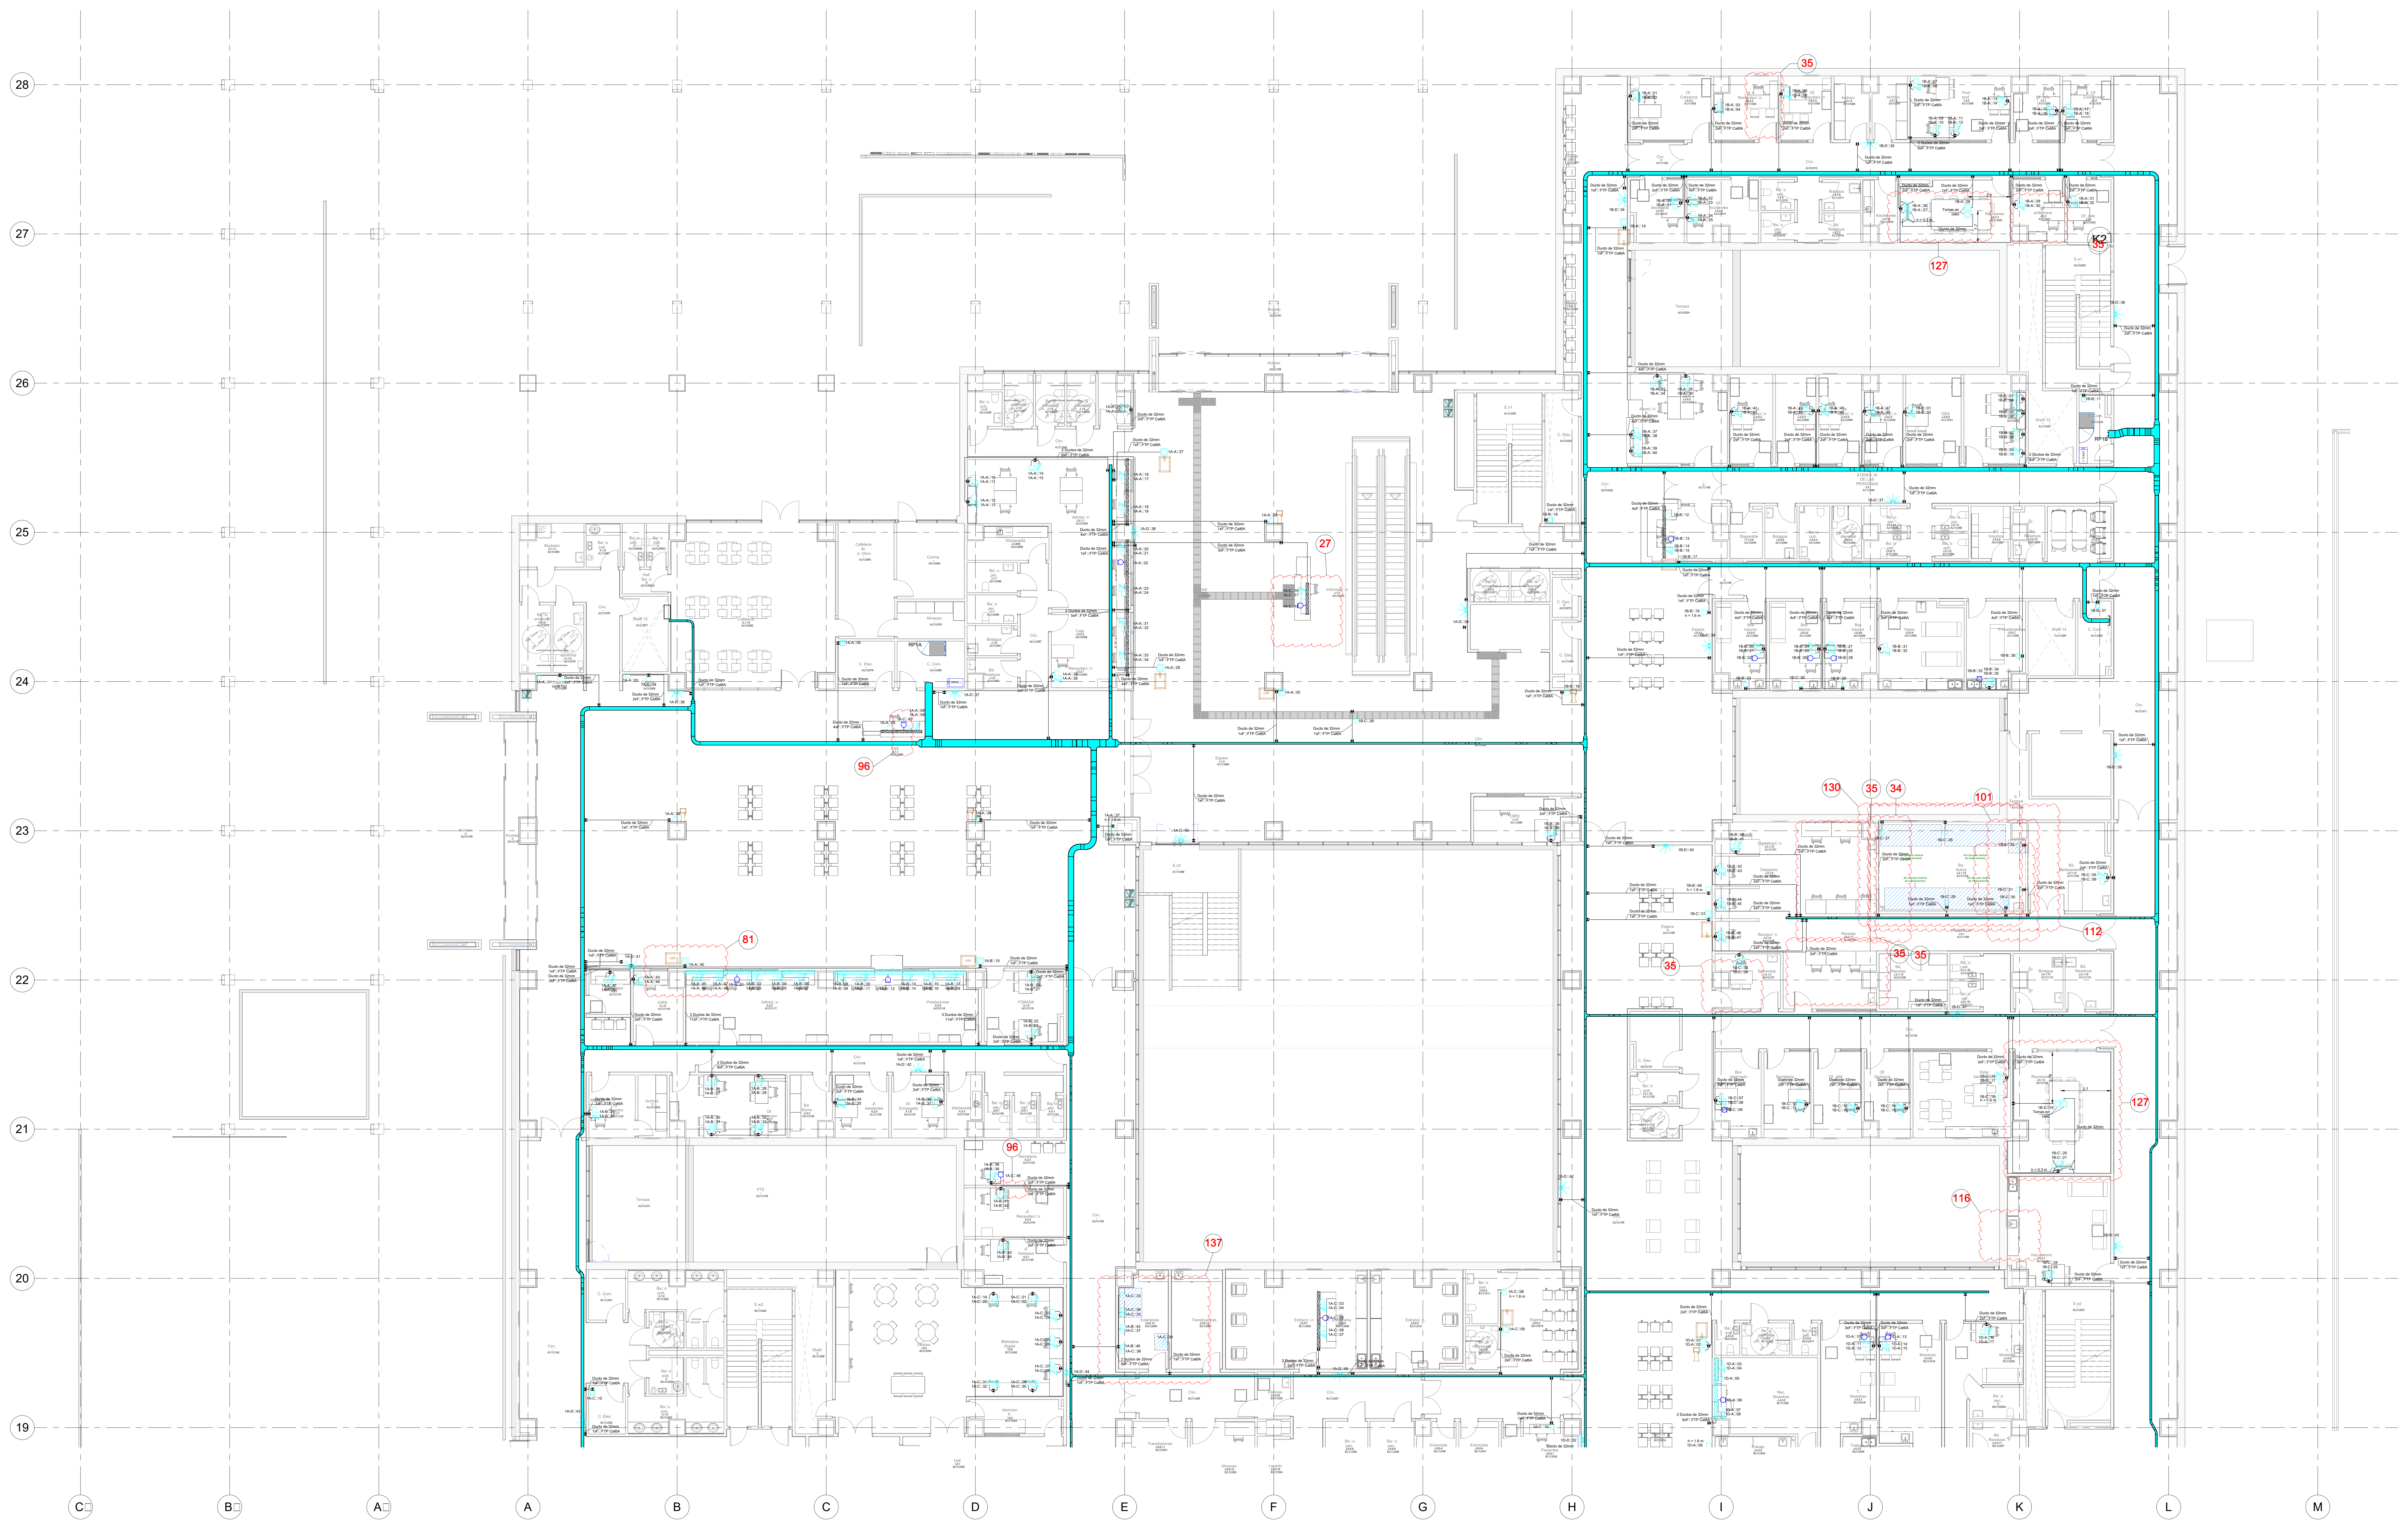

LEYENDA SISTEMA DE VOZ Y DATOS

d	TOMA DATOS COMPUTACIÓN RJ-45 FTP Cat.6A A UNA ALTURA DE 0.3M
D	TOMA DATOS COMPUTACIÓN FTP RJ-45 Cat.6A DE MONTAJE EN CIELO
H	CONJUNTO DE TOMAS AUDIOVISUALES HDMI Y USB DE MONTAJE EN PARED
H	CONJUNTO DE TOMAS AUDIOVISUALES HDMI Y USB DE MONTAJE EN CIELO
B	TOMA DE DATOS PARA SISTEMA DE CONTROL BMS RJ-45 FTP Cat. 6A
S	TOMA DE DATOS PARA SENSOR SÍSMICO
d▽	TOMA DATOS □ TELÉFONO IP FTP RJ-45 Cat.6A A UNA ALTURA DE 0.3m
▽	TOMA TELÉFONO ASCENSOR FTP RJ-45 Cat.6 EN CUADRO DE MANIOBRA ASCENSOR
▨	TOMA TELÉFONO PÚBLICO FTP RJ-45 Cat.5e
▬	BANDEJA PORTACONDUCTORES DE PLÁSTICO 150X65MM PARA MONTAJE SOBREPUESTO DE AVANCE POR ZÓCALO O MOBILIARIO.
	PUNTO DE ACCESO WIFI MONTADO EN PARED A 2.5 METROS DE ALTURA
	REGISTRO DE ENLACE PARA ENTRADA EN EDIFICIO DE OPERADORES 450x450x150 mm
	ARMARIO RACK 19". DIMENSIONES INDICADAS EN ESQUEMA DE DETALLES.
⊠	CAJA DE DISTRIBUCIÓN 100x100x50 mm
—	DUCTO DE 32 mm
▬	BANDEJAS. DIMENSIONES SEGÚN PLANOS
	CABECERO DE ZONAS CRÍTICAS
1	TIPO 1, CABECERO CLÍNICO INTEGRAL 1500 MM, DE EJECUCIÓN ADOSADA, EQUIPADO CON 4 TOMAS ELÉCTRICAS (2 TOMAS DE 10A, 1 DEL TIPO SCHUKO Y 1 PARA COMPUTACIÓN), 2 TOMAS DE VOZ Y DATOS, SISTEMA DE ALARMA DE PARO, 1 TOMA DE OXÍGENO, 1 TOMA DE VACÍO Y 1 TOMA DEAIRE MEDICINAL . USO EN ZONAS DE URGENCIA.
2	TIPO 2, CABECERO CLÍNICO INTEGRAL 1500 MM, DE EJECUCIÓN ADOSADA, EQUIPADO CON 4 TOMAS ELÉCTRICAS (2 TOMAS DE 10A, 1 DEL TIPO SCHUKO Y 1 PARA COMPUTACIÓN), 2 TOMAS DE VOZ Y DATOS, SISTEMA DE ALARMA DE PARO, SISTEMA DE ILUMINACIÓN DIRECTA E INDIRECTA CON INTERRUPTORES, 1 TOMA DE OXÍGENO, 1 TOMA DE VACÍO Y 1 TOMA DE AIRE MEDICINAL . USO EN SALAS DE RECUPERACIÓN QUIRÚRGICA.
3	TIPO 3, CABECERO CLÍNICO INTEGRAL 1500 MM, DE EJECUCIÓN ADOSADA, EQUIPADO CON 8 TOMAS ELÉCTRICAS (4 TOMAS DE 10A, 2 DEL TIPO SCHUKO Y 2 PARA COMPUTACIÓN), 2 TOMAS DE VOZ Y DATOS, SISTEMA DE AVISO A ENFERMERÍA CON TIRADOR, 2 TOMAS DE OXÍGENO, 2 TOMAS DE VACÍO Y 2 TOMAS DE AIRE MEDICINAL . USO EN SALAS DE PARTO.
4	TIPO 4, CABECERO CLÍNICO INTEGRAL 1500 MM, DE EJECUCIÓN ADOSADA, EQUIPADO CON 4 TOMAS ELÉCTRICAS (2 TOMAS DE 10A, 1 DEL TIPO SCHUKO Y 1 PARA COMPUTACIÓN), 2 TOMAS DE VOZ Y DATOS, SISTEMA DE AVISO A ENFERMERÍA CON TIRADOR, SISTEMA DE ILUMINACIÓN DIRECTA E INDIRECTA CON INTERRUPTORES Y CONMUTADOR PARA LUZ TECHO, 1 TOMA DE OXÍGENO, 1 TOMA DE VACÍO Y 1 TOMA DE AIRE MEDICINAL . USO EN ÁREAS DE HOSPITALIZACIÓN CUIDADOS BÁSICOS.
5	TIPO 5, CABECERO CLÍNICO INTEGRAL 1500 MM, DE EJECUCIÓN ADOSADA, EQUIPADO CON 8 TOMAS ELÉCTRICAS (4 TOMAS DE 10A, 2 DEL TIPO SCHUKO Y 2 PARA COMPUTACIÓN), 2 TOMAS DE VOZ Y DATOS, SISTEMA DE AVISO A ENFERMERÍA CON TIRADOR, SISTEMA DE ILUMINACIÓN DIRECTA E INDIRECTA CON INTERRUPTORES Y CONMUTADOR PARA LUZ TECHO, 2 TOMAS DE OXÍGENO, 2 TOMAS DE VACÍO Y 2 TOMAS DE AIRE MEDICINAL . USO EN ÁREAS DE HOSPITALIZACIÓN CUIDADOS MEDIOS.
	PANEL DE CONTROL

SISTEMA DE ATENCIÓN POR TURNOS Y MÓDULOS

LCD	DISPLAY DE TURNOS CON CONEXIÓN A RED DE DATOS
	DISPENSADOR DE TICKETS CON CONEXIÓN A RED DE DATOS

NOTAS GENERALES

TODOS LOS CUADROS DE CONTROL CENTRALIZADO INCORPORARÁN SWITCHES CARRIL DIN, CON LAS SALIDAS SUFICIENTES PARA RECOGER TODAS LAS SEÑALES DE DATOS DE LAS MANEJADORAS Y CUADROS ELÉCTRICOS

TODO EL EQUIPAMIENTO FIJADO EN LOSA DEBERÁ CUMPLIR CON LOS REQUERIMIENTOS PARA ZONA SÍSMICA V4.

LAS TOMAS HDMI Y USB DE LAS SALAS DE REUNIONES ESTARÁN UNIDAS MEDIANTE CABLES MACHO-MACHO PRECONECTORIZADOS HDMI Y USB CON LA LONGITUD ADECUADA (CONSIDERANDO LA TOMA EN CIELO A UNA COTA DE 3 m Y DEJANDO UNA HOLGURA DE 0.5 m) Y CANALIZACIÓN MEDIANTE TUBO PVC CONDUIT Ø40mm.

N°	CAMBIOS RESPECTO VERSIÓN ANTERIOR	FECHA
137	COORDINACIÓN PME	27□04□2020
130	INCIDENCIA 1025□ COORDINA INSTALACIÓN VD EN BODEGA ACTIVA	16□04□2020
127	NC 2043□ COORDINACIÓN TOMAS HDMI P□RA RECINTOS EN QUE APLICAN	01□04□2020
116	REVISIÓN PME	09□03□2020
112	REVISIÓN PME	17□02□2020
101	REVISIÓN PME	05□02□2020
96	SDI 1198□ AJUSTE ETIQUETAS	23□10□2019
81	RAO 276□ CAMBIO TOMAS DATOS DISPLAYS DE TURNOS A CIELO	18□07□2019
65	COORDINACIÓN CON MOBILIARIO P1	20□02□2019
35	SE AGREGA□DESPLAZA VOY Y DATO, PARA COORDINACIÓN CON MOA	06□09□2018
34	SE DESPLAZA VOZ Y DATO, PARA AJUSTE COORDINACION CON PME	21□08□2018
28	ACTUALIZACIÓN DE BANDEJAS POR COORDINACIÓN	22□06□2018
27	RAO-077□ SE INCLUYE PUESTO DE TRABAJO EN MESÓN DE INFORMACIÓN	22□06□2018

TABLA DE CAMBIOS

Proyecto

NORMALIZACIÓN HOSPITAL PROVINCIAL DE CURICÓ

Dirección

RÍO ELQUI S□N - CURICÓ - REGIÓN DEL MAULE - ROL SII N° 638-99

Fase

FASE 03

Título de plano

SISTEMA DE VOZ Y DATOS. PLANTA PISO 1 - SECTOR 1

Especialidad

CABLEADO ESTRUCTURADO Y CORRIENTES DÉBILES

Especialista

JUAN C. MELET FRIZ

Código de plano

HCU-DEB-VD-101

Archivo□Formato

HCU-DEB-VD-101.dwg
A0□□ 841x1689

Fecha

27□04□2020

Revisión

07.10

Escala

0 1 2 3 4 5

1□100

Jefe de proyecto

JUAN CASARIEGO
CÓRDOBA
ARQUITECTO

Propietario

SERVICIO DE SALUD DEL MAULE
RODRIGO ALARCÓN QUESEM
DIRECTOR
REPRESENTANTE LEGAL SERVICIO DE SALUD DEL MAULE
RUN 9.064.078-K

Empresa Constructora

OBRASCÓN HUARTE LAIN S.A.
AGENCIA EN CHILE

Unidad Técnica

Dirección de Arquitectura
Ministerio de Obras Públicas
Gobierno de Chi

Propietario

Servi
Salud
Región
Minist
Salud

PLANO APTO PARA CONSTRUCCION

Revision	**V°B°**
07.10	

OFICINA TECNICA HCU OHL